


Перв. примен.	Справ. №	Подп. и дата	Инв. и дубл.	Взам. инв. №	Подп. и дата	Инв. № подл.

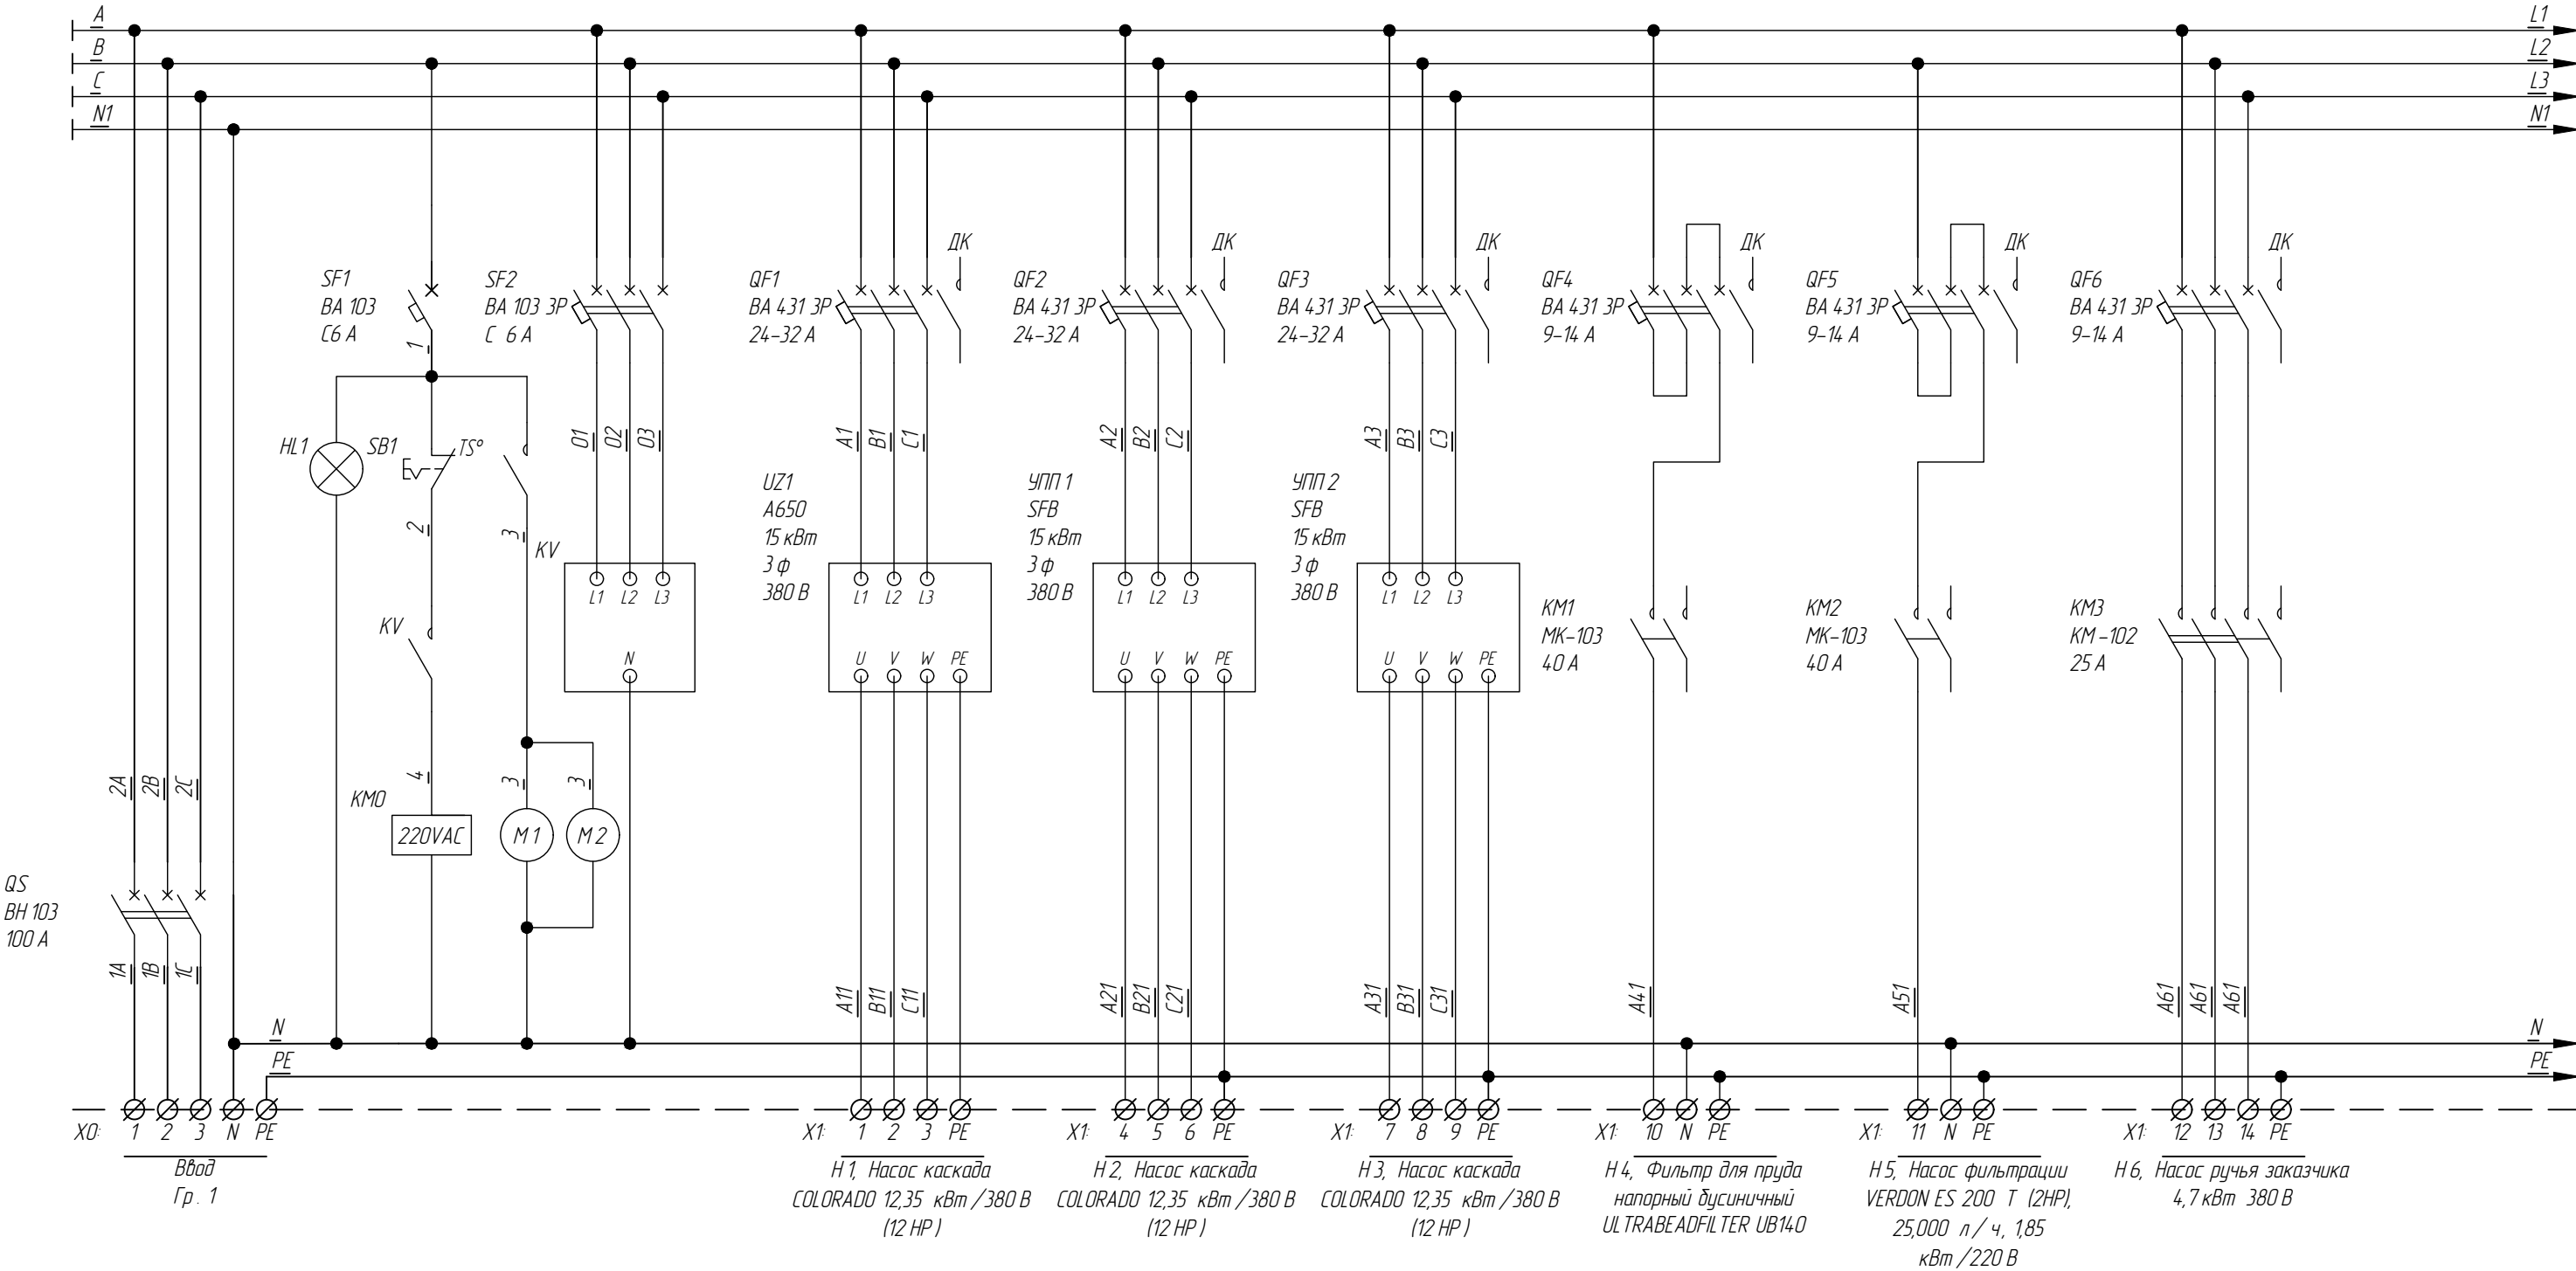


Примечания :
Допускается замена проектируемого оборудования на аналогичное по эксплуатационным характеристикам, климатическому исполнению и категории размещения соответствующее местам установки и не ухудшающее эксплуатационных характеристик . При этом согласования с разработчиками документации не требуются , изменения в документацию не вносятся .

						25-01-2001			

Изм.	Кол.уч	Лист	№ док	Подпись	Дата	Фонтан интерьерный .	Стадия	Лист	Листов
Разработал	Дреннов						Р	1	8
Проверил	Поликарпов								
Утвердил	Поликарпов					Схема принципиальная ЩУ			

[illegible]

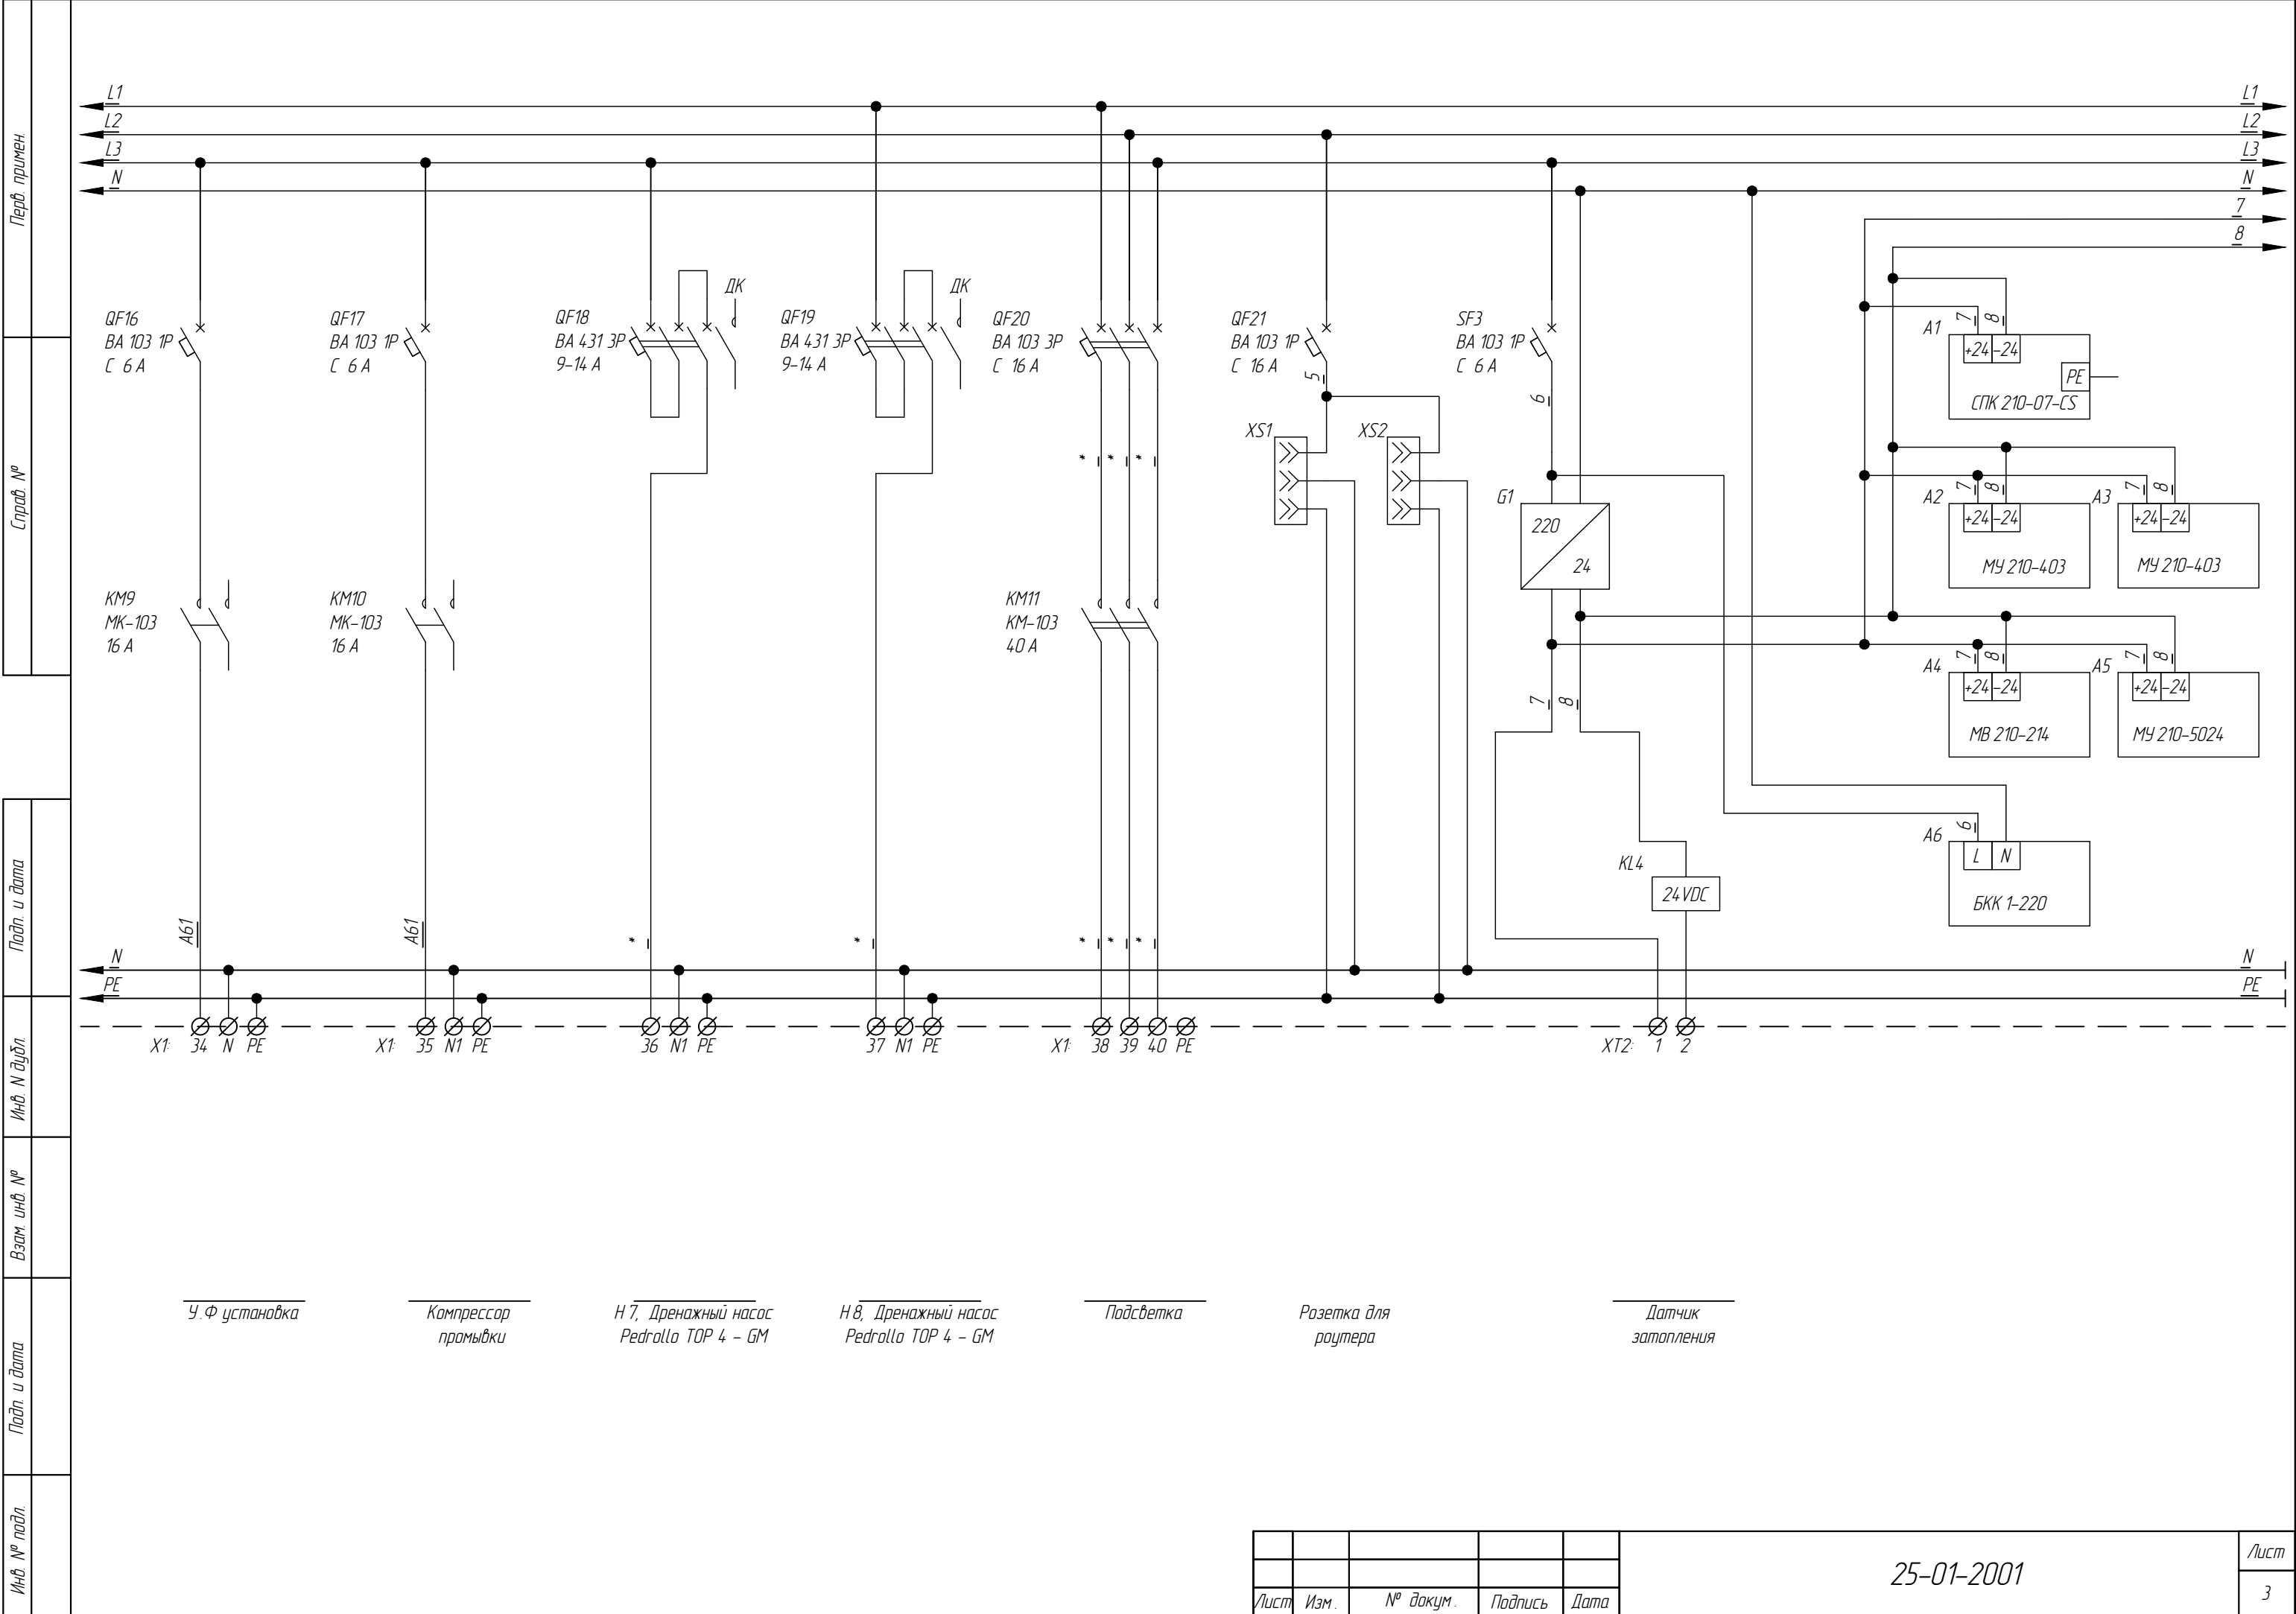

Перв. примен.

Справ. №

Подп. и дата

Инв. и дудл.

Взам. инв. №

Подп. и дата

Инв. № подл.

Лист

4

Л1
Л2
Л3
N

A2

SF4
BA 103 1P
C 6 A

KMO
KM-103
16 A

12 10 14 16 11 18 20 10 22 24 10 26

1 2 3 4 5 6 7 8 9 10 11 12

001B 001,2A 002B 003B 003,4A 004B 005B 005,6A 006B 007B 007,8A 008B

Ручн. вкл. Автомат

SA1 SA2 SA3 SA4 SA5 SA6 SA7 SA14

11 13 15 17 19 21 23 25

KL1 HL1 KL2 HL2 KL3 HL3 KM1 HL4 KM2 HL5 KM3 HL6 KM4 HL7 KM11

220VAC

N
PE

N
PE

Н 1, Насос каскада
COLORADO 12,35 кВт /380 В
(12 HP)

Н 2, Насос каскада
COLORADO 12,35 кВт /380 В
(12 HP)

Н 3, Насос каскада
COLORADO 12,35 кВт /380 В
(12 HP)

Н 4, Фильтр для пруда
напорный бесшумный
ULTRABEADFILTER UB140

Н 5, Насос фильтрации
VERDON ES 200 T (2HP),
25,000 л / ч, 1,85
кВт /220 В

Н 6,
Насос ручья заказчика

М 1,
Генератор тумана

Подсветка

25-01-2001

Лист


Изм.

№ докум.

Подпись

Дата

Инд. № подл.	Подп. и дата	Взам. инд. №	Инд. N дудл.	Подп. и дата

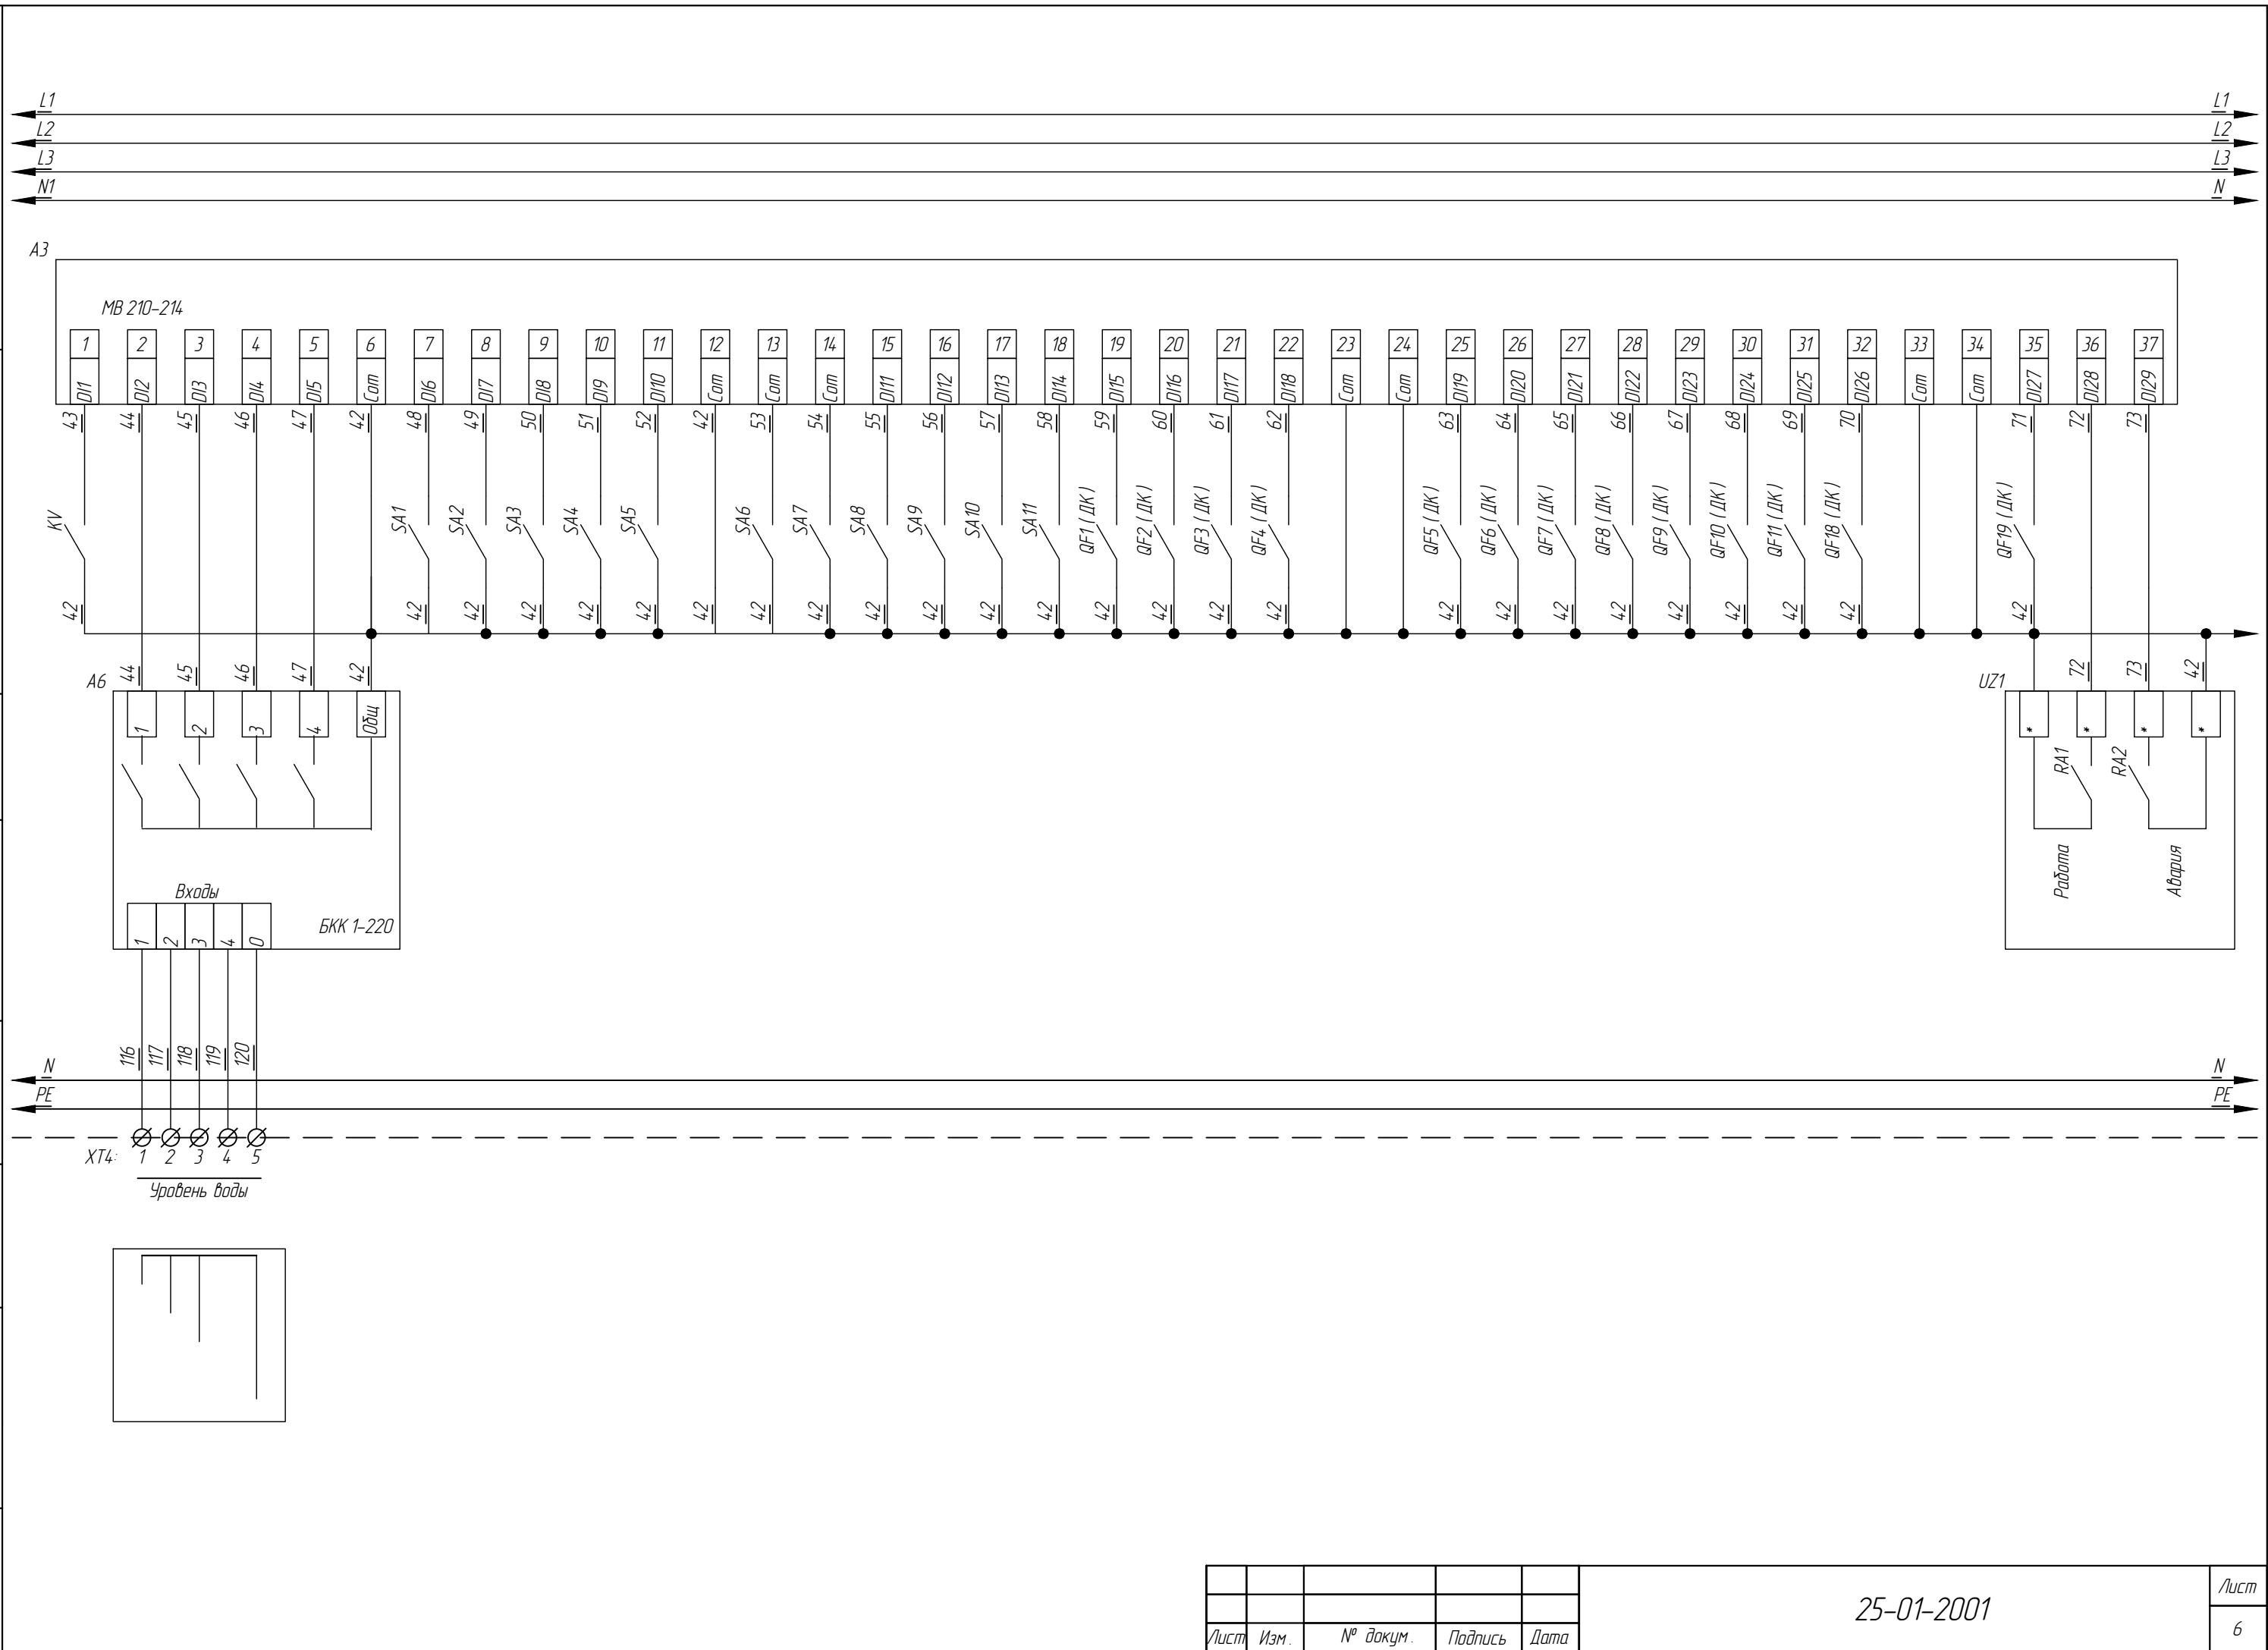

					25-01-2001	Лист
						6
Лист	Изм.	№ докум.	Подпись	Дата		

Схематический чертеж электрической цепи, включающий силовую часть, цепи управления и цепи сигнализации.

Силовая часть:

- Входные линии: $L1$, $L2$, $L3$, $N1$.
- Терминалы: 38, 39, 40 (D130, D131, D132) и 1-30 (D11-D124).
- Оборудование: MB 210-214.
- Средства защиты: КМ0, КМ1, КМ2, КМ3, КМ4, КМ5, КМ5.1, КМ6, КМ6.1, КМ7, КМ8, КМ9, КЛ4, УФ, КМ10.
- Соединения: 74, 75, 76, 77, 78, 79, 80, 81, 82, 83, 84, 85, 86, 87, 88, 89, 90, 91, 92, 93, 94, 95, 96, 97, 98, 99, 100, 101.

Цепи управления:

- УПП 1: 4 (Работа), 5 (Авария), 7, 6.
- УПП 2: 4 (Работа), 5 (Авария), 7, 6.

Цепи сигнализации:

- Терминалы: 1-16 (X15).
- Состояния: M2, M3, M4, M5 (Закрыта, Открыта).

Таблица данных:

Лист	Изм.	№ докум.	Подпись	Дата
25-01-2001				

Лист 7

